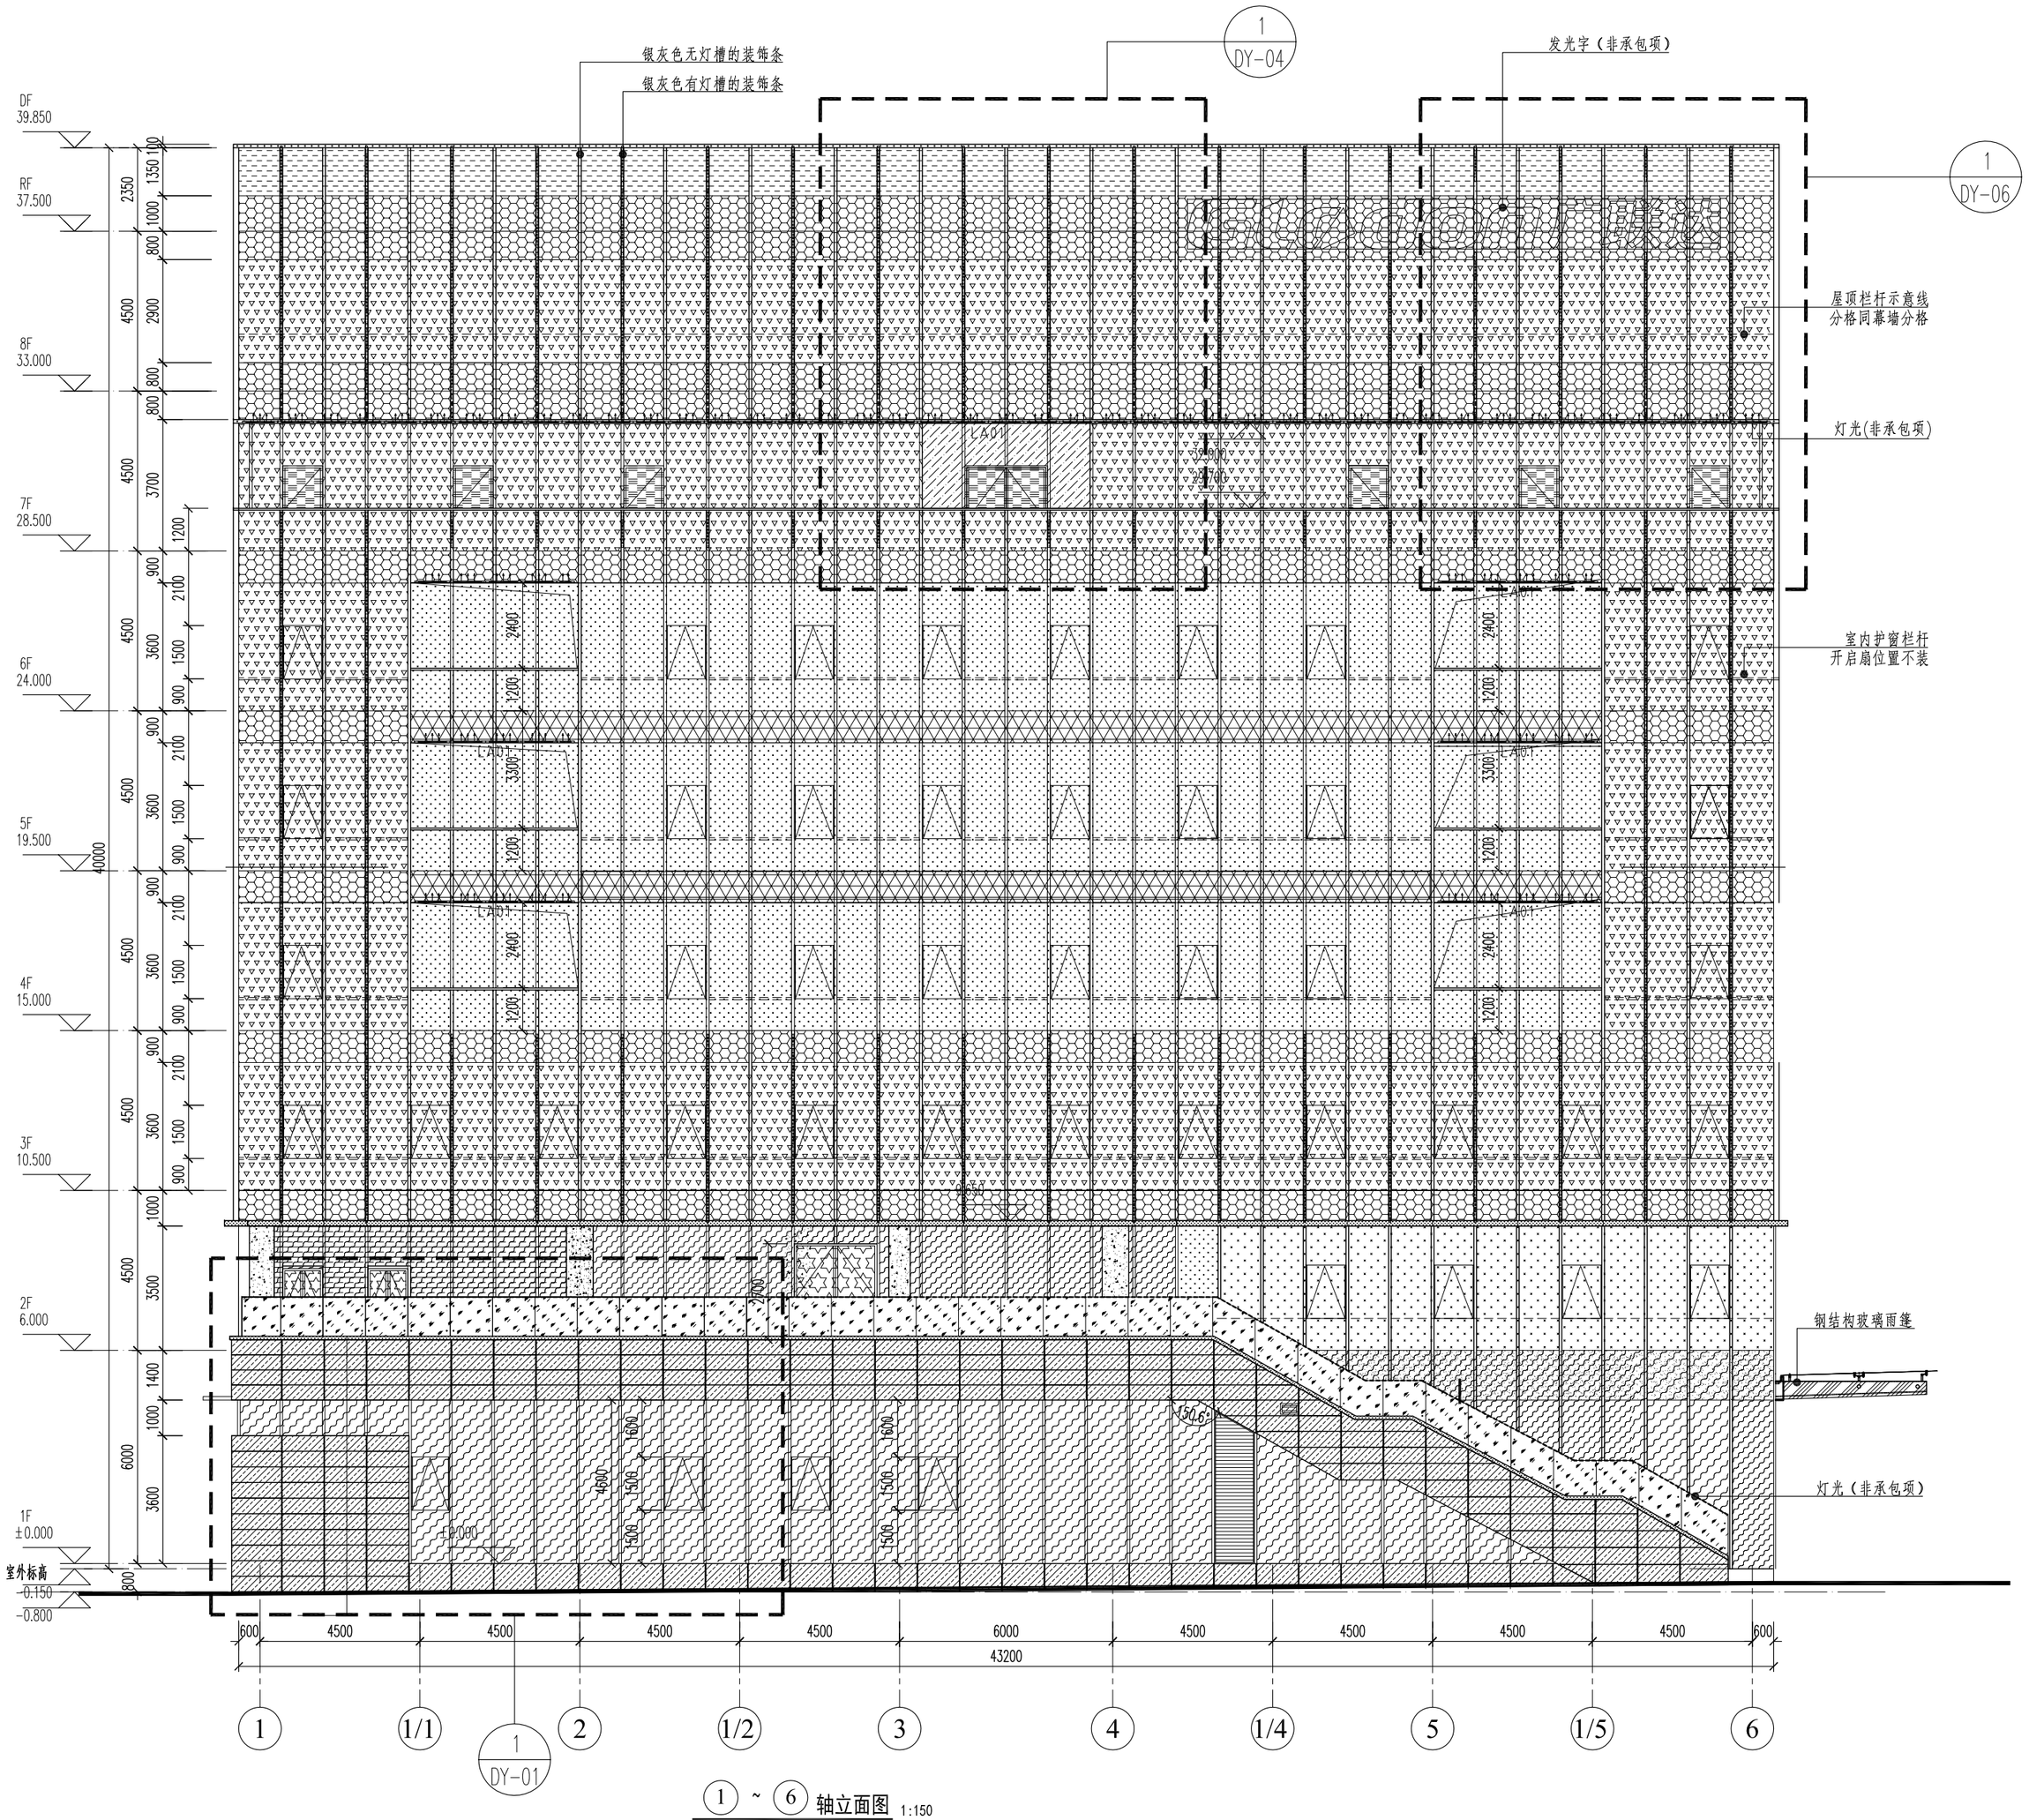


① ~ ⑥ 轴立面图 1:150

石材横缝密缝6mm
石材横缝缝宽10mm
石材竖缝缝宽20mm

图例：

8+1.52PVB+8+12(空气)+10三银Low-e夹胶中空超白半钢化玻璃 （蓝灰色）	8+1.52PVB+8+12(氩气)+10三银Low-e夹胶中空超白(高透)半钢化玻璃	10+12Ar+10三银Low-e中空超白（蓝灰色）钢化玻璃	1.5mm不锈钢板
8+1.52PVB+8+12(氩气)+10三银Low-e夹胶中空超白半钢化玻璃 （蓝灰色）	6+1.52PVB+6+12(空气)+8三银Low-e夹胶中空超白(高透)半钢化玻璃+2mm铝背板(颜色待定)	8+1.52pvb+8mm钢化夹胶玻璃	8mm埃特板背衬(白色)
6+1.52PVB+6+12(空气)+8三银Low-e夹胶中空超白半钢化玻璃 （蓝灰色）+2mm铝背板(颜色待定)	8+12(氩气)+8三银Low-e超白（高透）中空钢化玻璃(逃生窗)	30mm厚浅灰色石材	铝百叶
8+12(氩气)+8三银Low-e超白中空钢化玻璃（蓝灰色）(逃生窗)	12+12(氩气)+12三银Low-e超白（高透）中空钢化玻璃	2.5mm厚银灰色铝单板	消防救援窗
10+1.52PVB+10超白（高透）钢化夹胶玻璃（电梯）	15mm厚单片超白（高透）钢化玻璃（门玻） 15mm厚单片超白（蓝灰色）钢化玻璃（门玻）	2.5mm厚木纹铝单板（天花）	2mm厚铝背板（灰色）

广州珠江装修工程有限公司
GUANGZHOU PEARL RIVER DECORATION ENGINEERING CO., LTD.
地址：广州市建设五马路29号 邮编：510060
电话：020-83850380 传真：83819240

备注：
所有尺寸必须在工地现场量度。图纸尺寸大小以所注为依据，不可用比例尺直接量度，本图册及其副本均为广州珠江装修工程公司之版权所有，翻印必究。

工程项目 PROJECT
广联达科技股份有限公司 智慧建造总部基地（华南总部基地）项目

业务号 JOB NO

图纸名称 DRAWING TITLE
① ~ ⑥ 轴立面图

图号 DRAWING NO.
LM-01

修订 Rev.	日期 Date	备注 Note

项目负责人 DIRECTED BY	陈中正	
设计 DESIGNED BY	黄继发	
绘图 DRAWN BY	黄继发	
校核 REVIEWED BY	李志运	
审核 CHECKED BY	陈中正	
审定 SIGNED BY		

图类 DWG TYPE 施工图 | 专业 SUBJECT 幕墙

日期 DATE 2023.07